



VAR
21° W (2002)

METERS

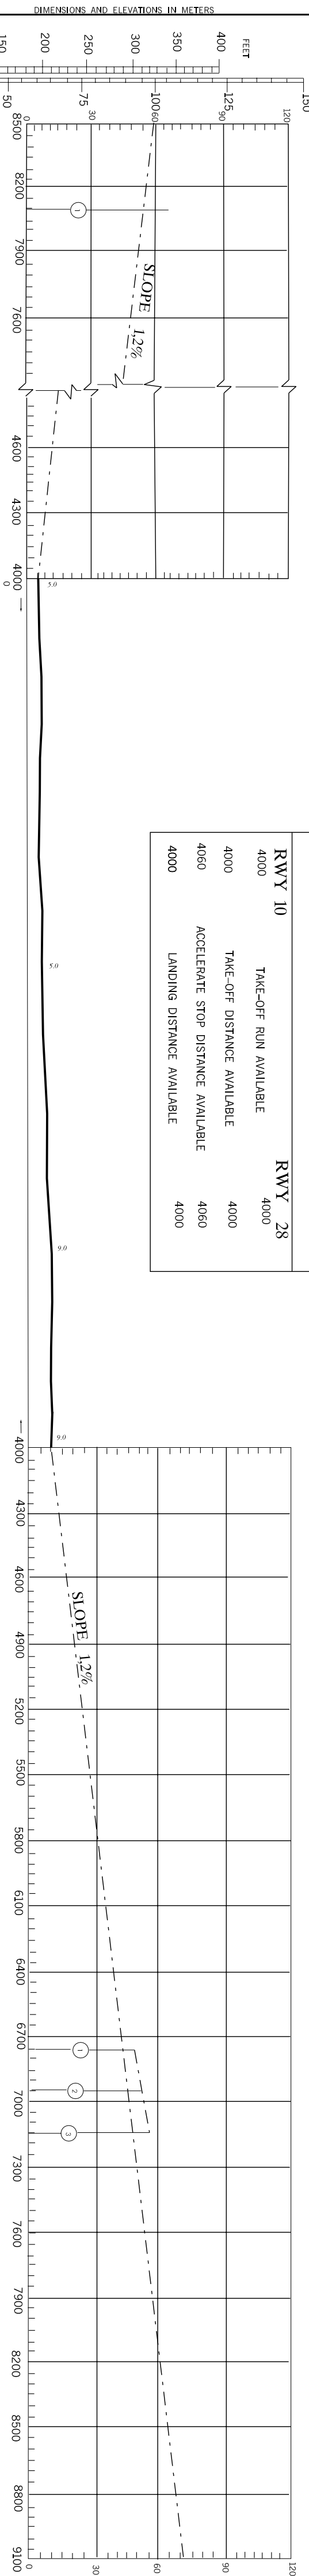


DECLARED DISTANCE			
RWY 10	TAKE-OFF RUN AVAILABLE	RWY 28	TAKE-OFF RUN AVAILABLE
4000	4000	4000	4000
4000	TAKE-OFF DISTANCE AVAILABLE	4000	TAKE-OFF DISTANCE AVAILABLE
4060	ACCELERATE STOP DISTANCE AVAILABLE	4060	ACCELERATE STOP DISTANCE AVAILABLE
4000	LANDING DISTANCE AVAILABLE	4000	LANDING DISTANCE AVAILABLE

VERTICAL SCALE
1:2,000

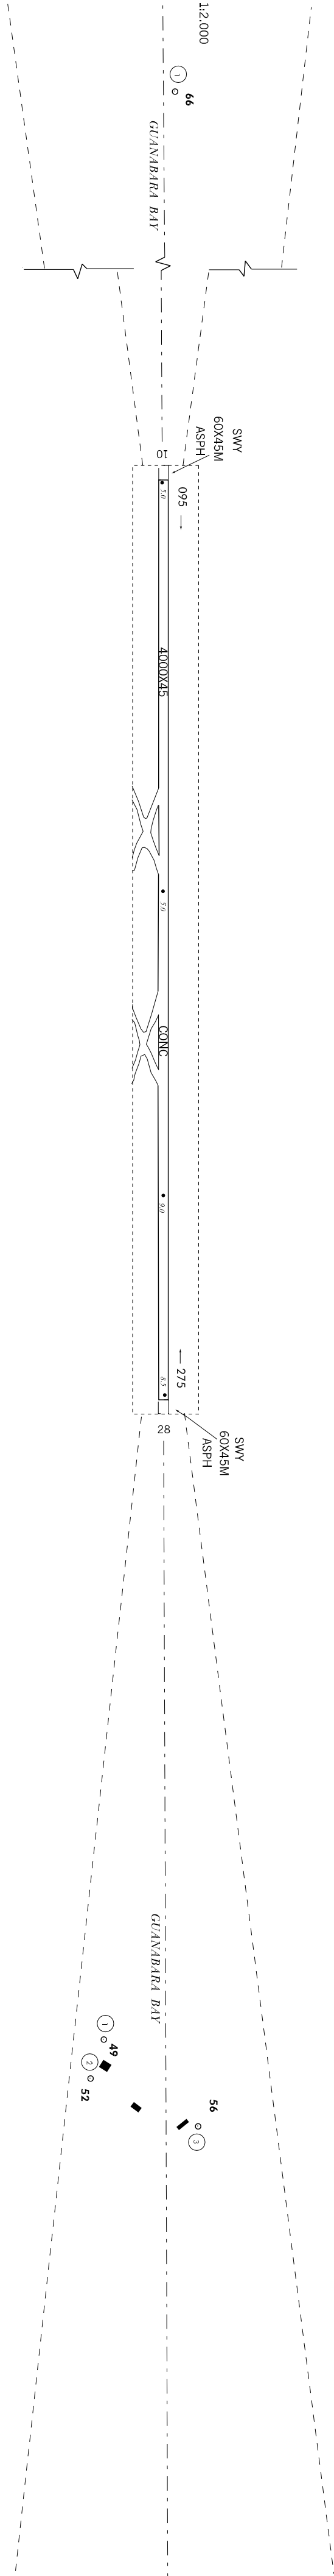

LEGEND	
IDENTIFICATION NUMBER	①
BUILDING OR LARGE STRUCTURE	■
POLE, TOWER, ANTENNA, ETC..	○

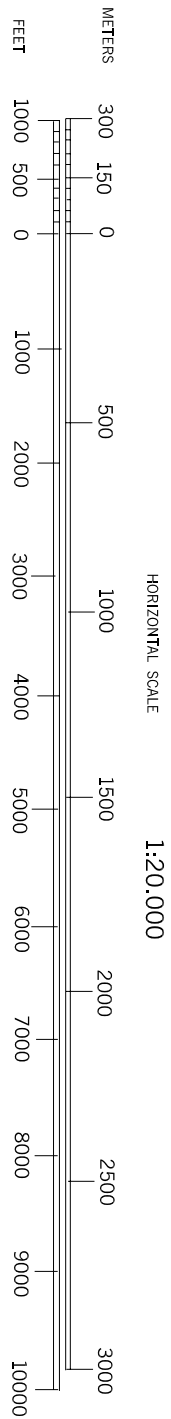

AMENDMENT RECORD		
Nº	DATE	ENTERED BY

COMAER

CHANGES: TDZ.

AIP AMDT 08/12